



POCKET STUDIO · A VANCOUVER R1-1 ZONING LANEWAY HOUSE TESTER

2893 E 49TH AV


R1-1 laneway house · two storey 2-bed · October 2, 2026

LOT	13.5 × 55.9 m · 701.2 m² · R1-1
LANEWAY HOUSE	two storeys · 60.2 m² ground + 35.8 m² upper = 96.0 m²
FLOOR-AREA CAP	175.3 m² (s.11.3.8.2)
HEIGHT	8.4 m of 8.5 m · gable (ridge along depth) roof
SITE COVERAGE	39.5 % of 50 %
SEPARATION	4.9 m (min 4.9)
LAYOUT	2-bed · two storey · 88 m²
MATERIALS	Cedar, vertical light · Asphalt shingle
OPENINGS	10 windows · 1 door(s)
COMPLIANCE	all requirements met

- City of Vancouver Zoning & Development By-law, R1-1 District Schedule
- Missing Middle report, App. A, s.11.3.8
- BCBC 9.8 stairs

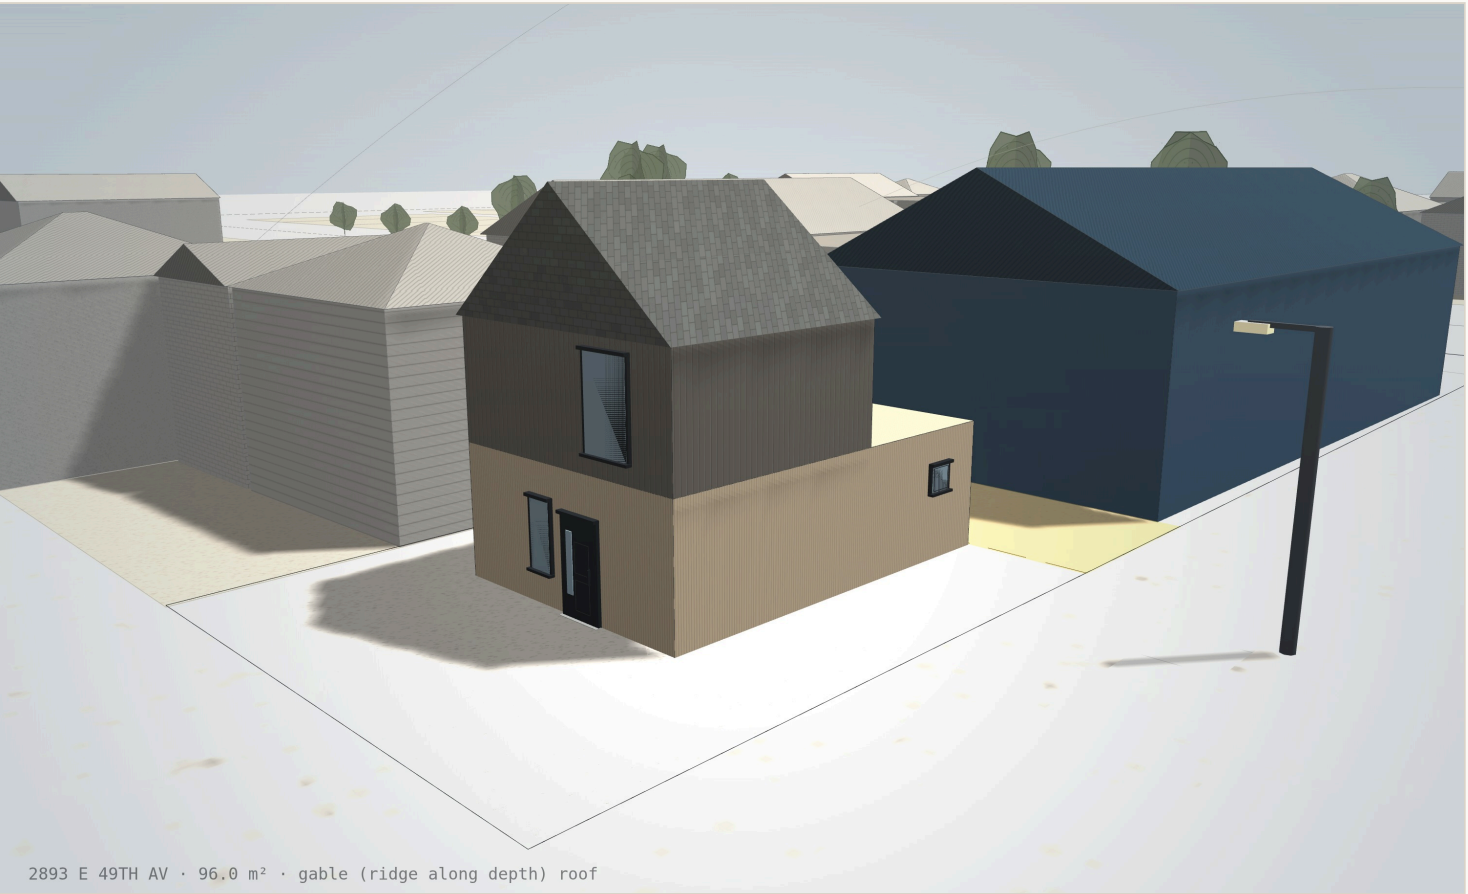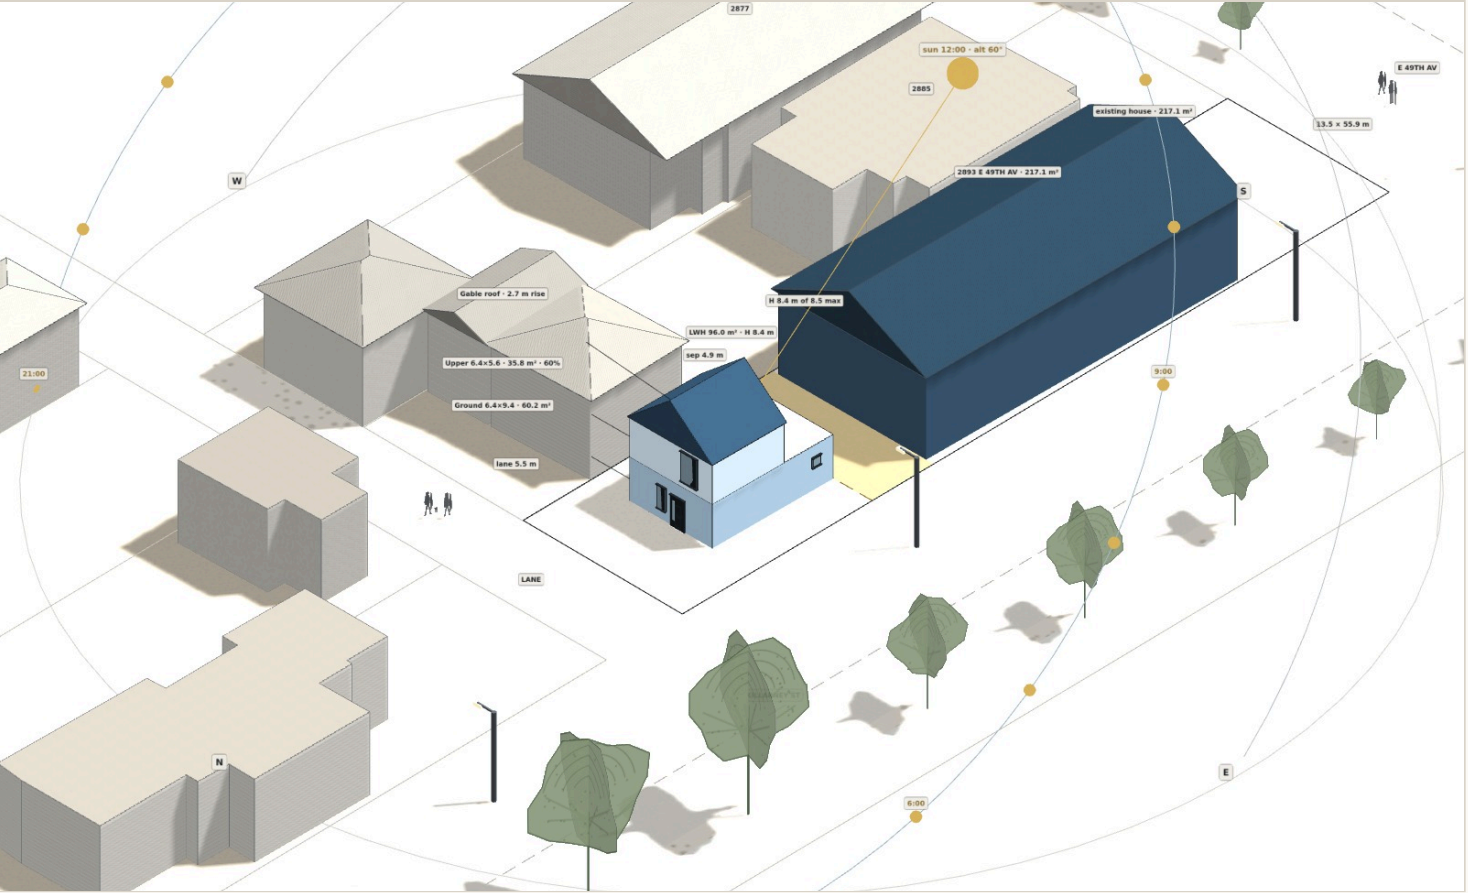


2893 E 49TH AV · 96.0 m² · gable (ridge along depth) roof

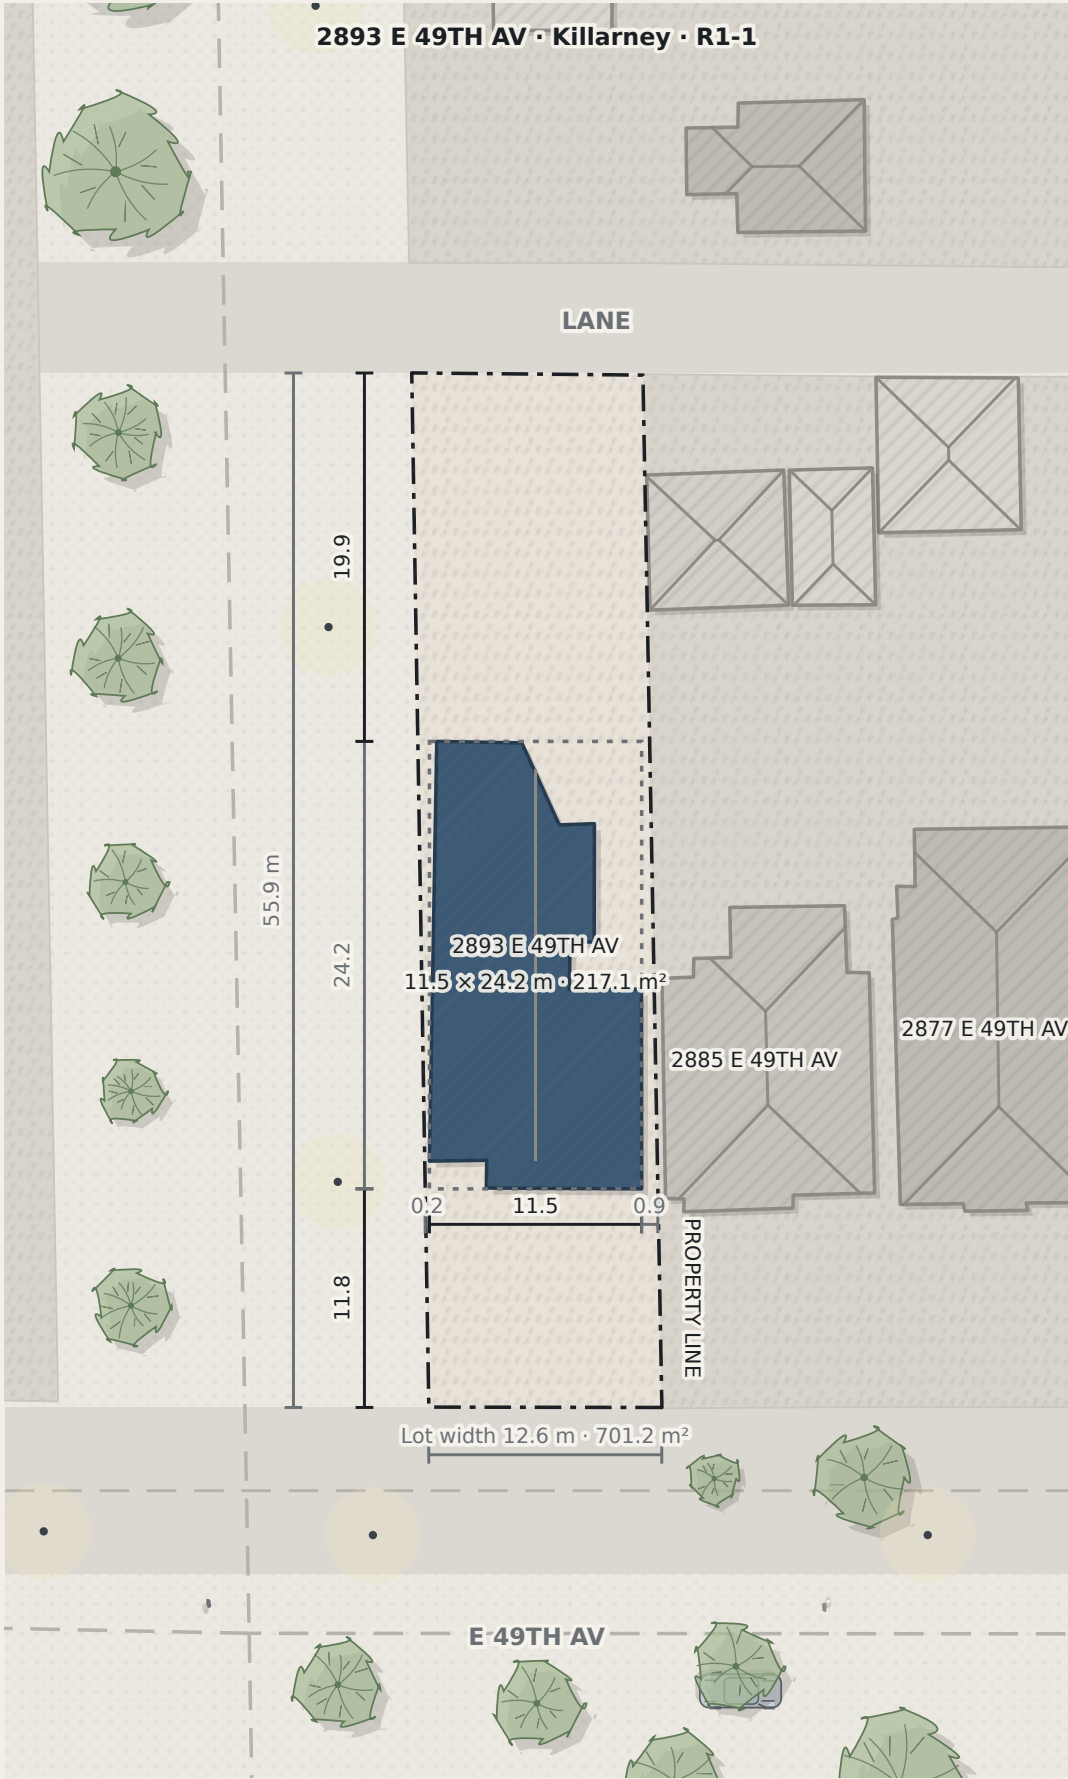

Existing lot plan
2893 E 49TH AV

0 5 m


N

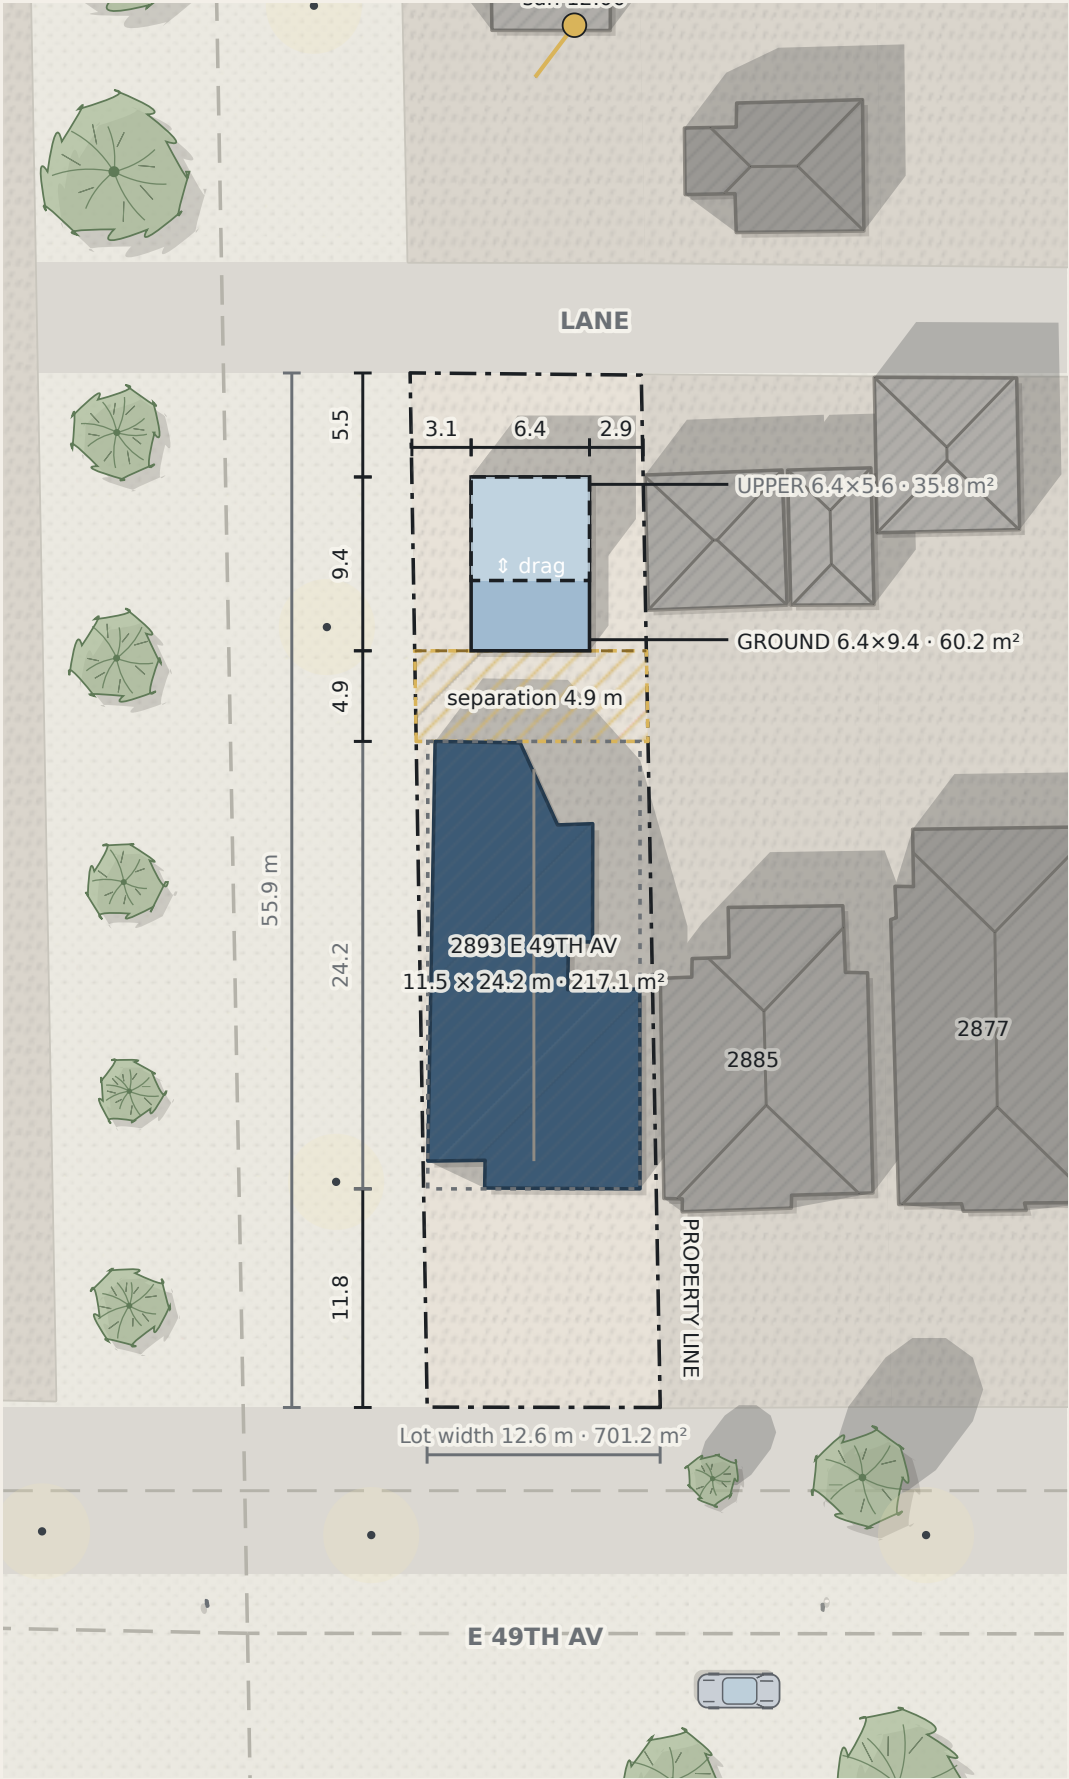

Site plan
2893 E 49TH AV · laneway house · setbacks in m


0 5 m

N

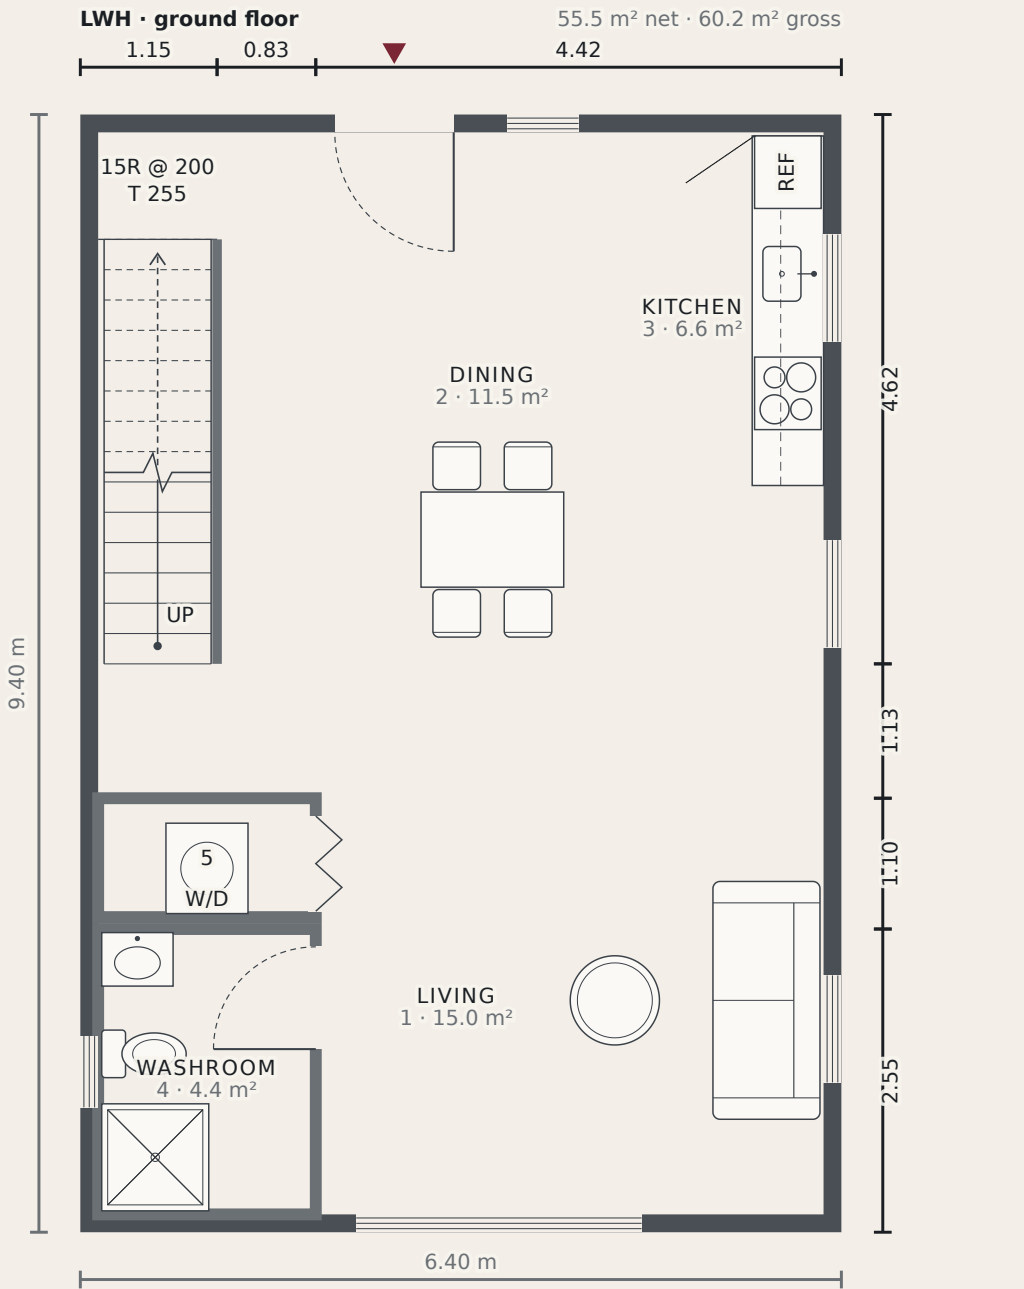

2-bed · ground floor plan




2893 E 49TH AV · two storey · 88 m²


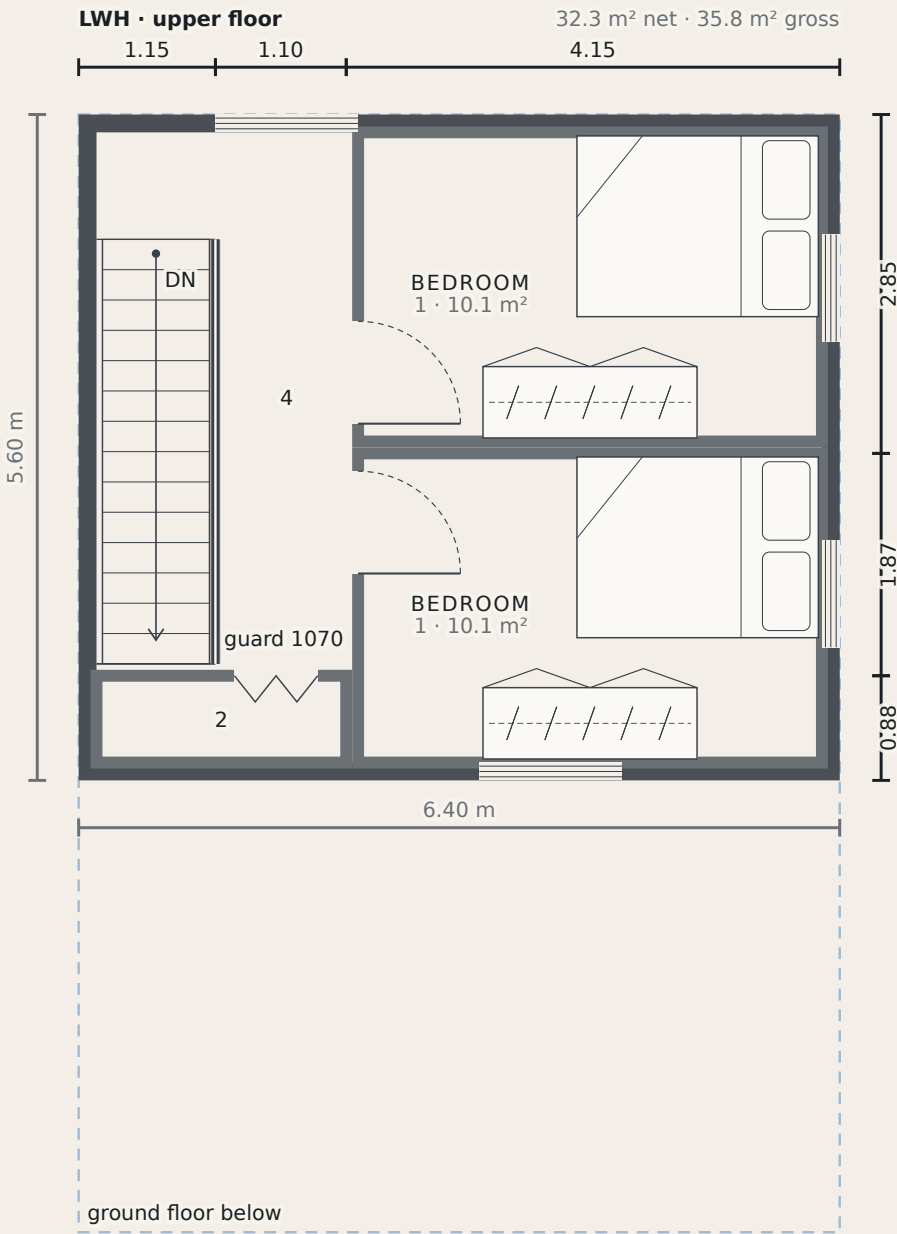


2-bed · upper floor plan


2893 E 49TH AV · two storey · 88 m²



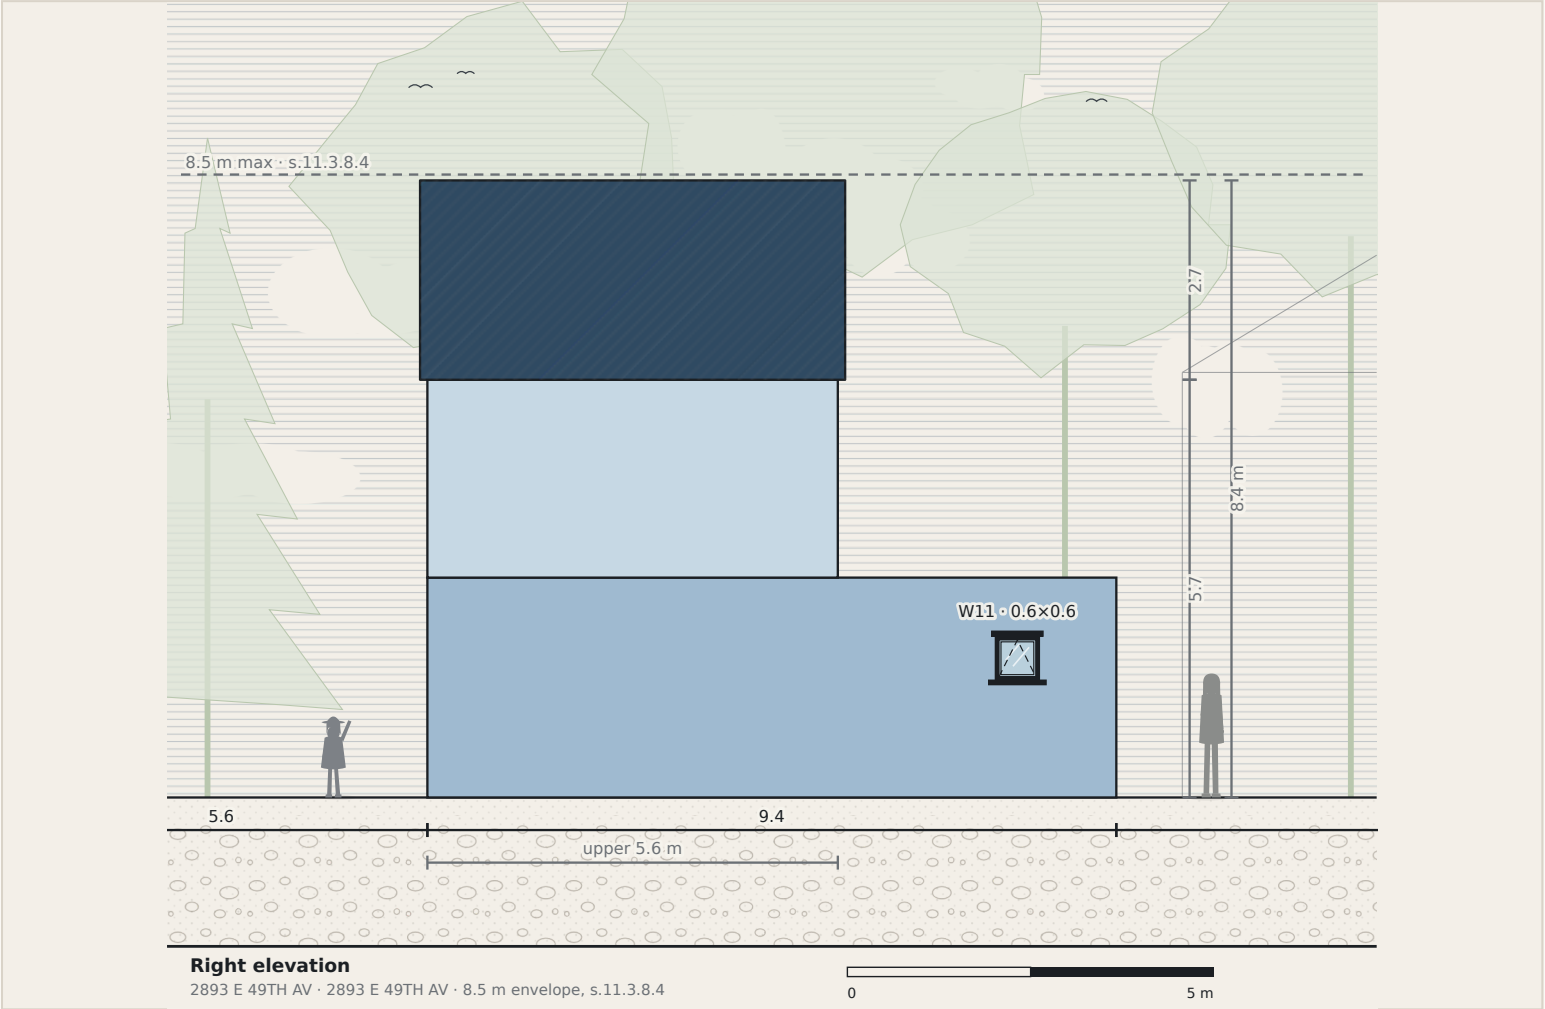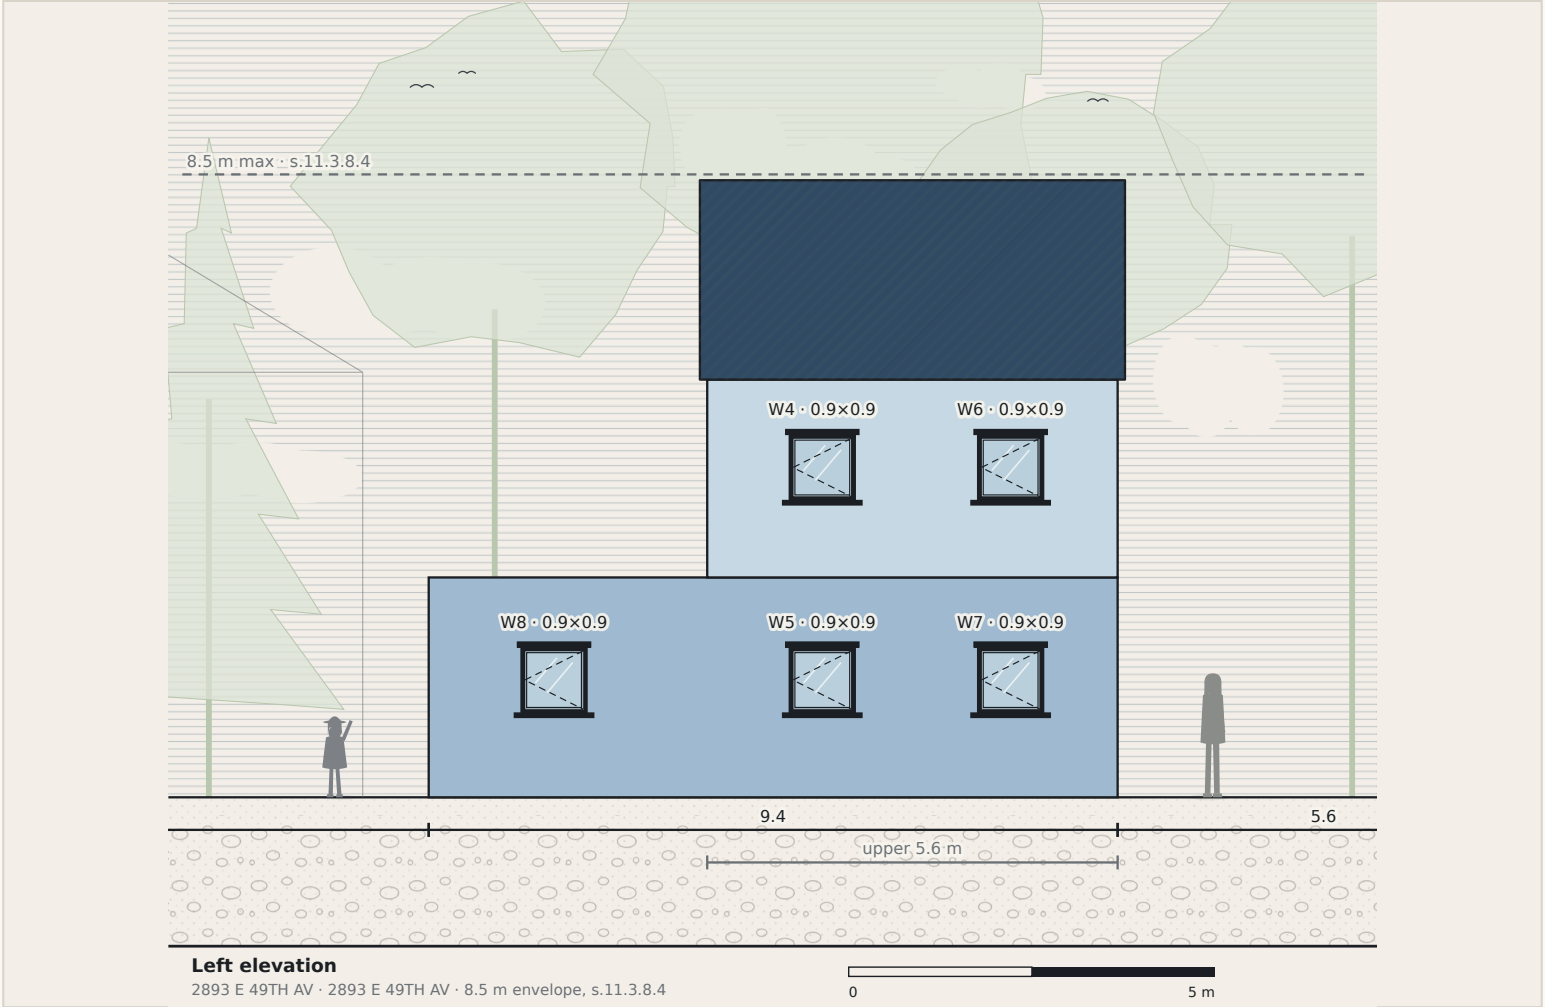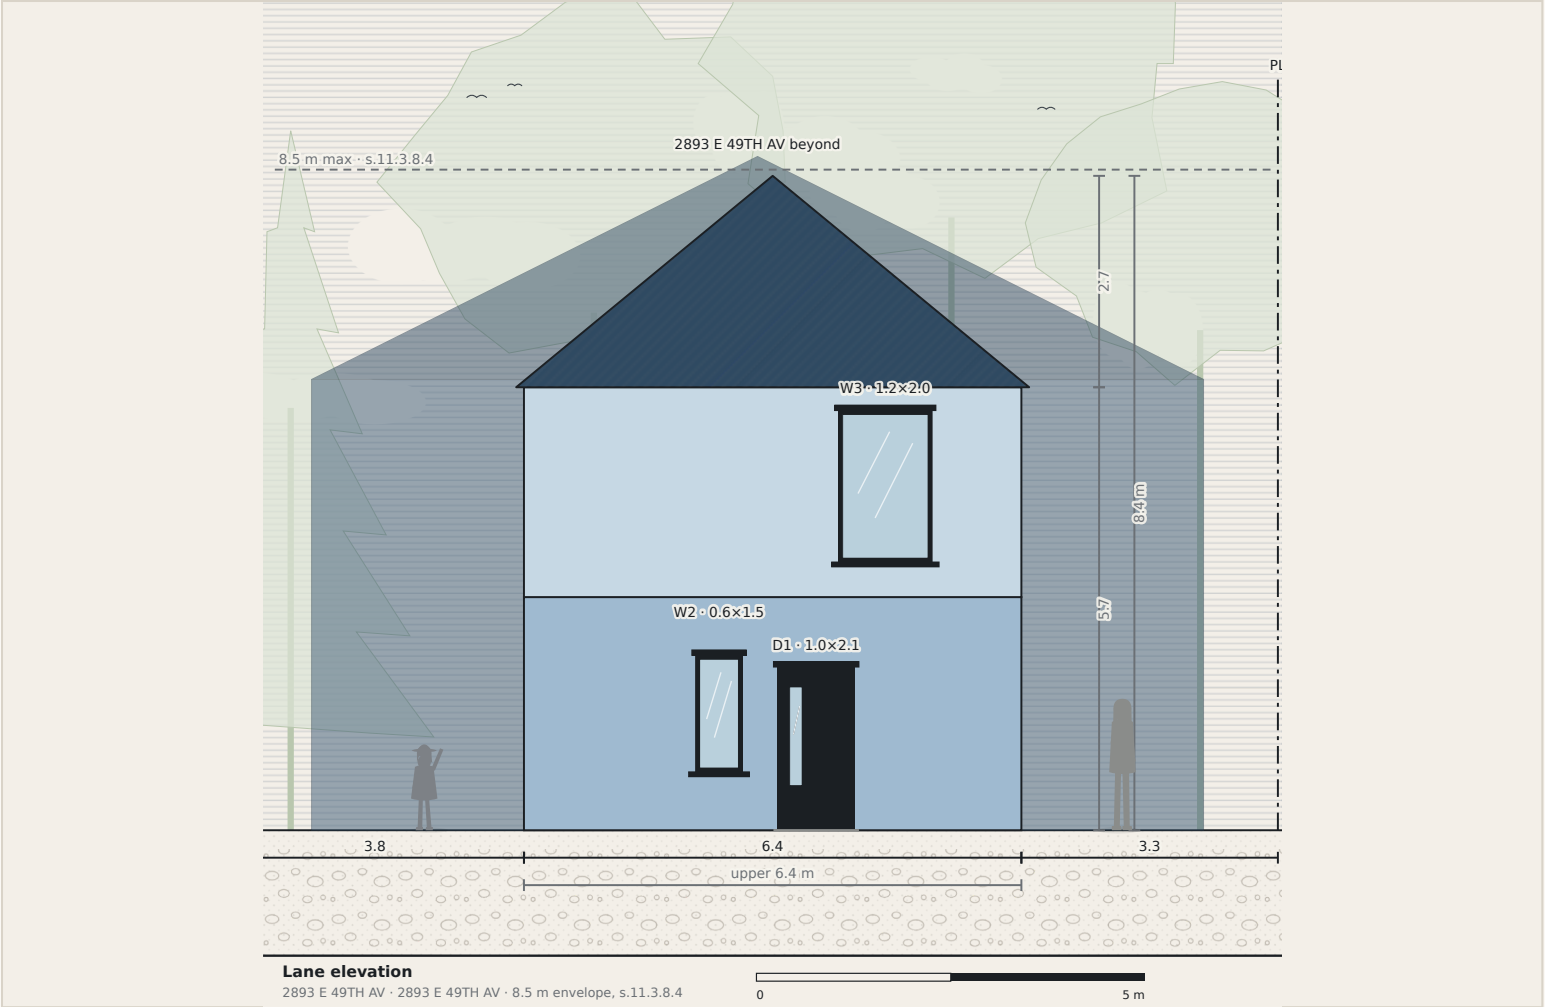

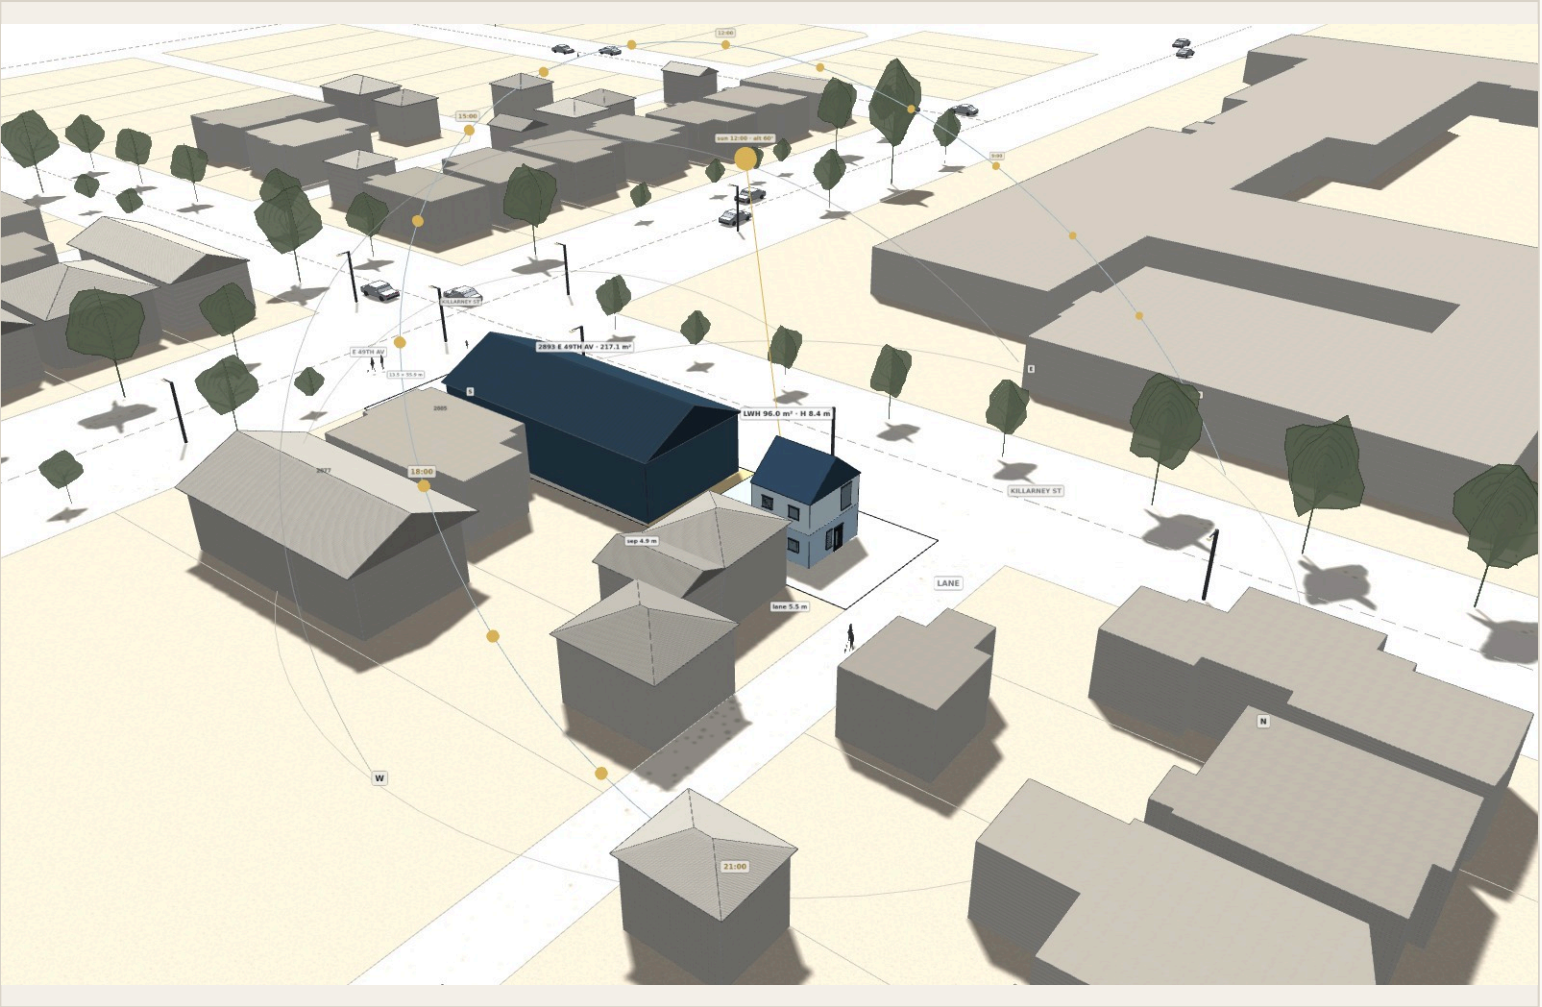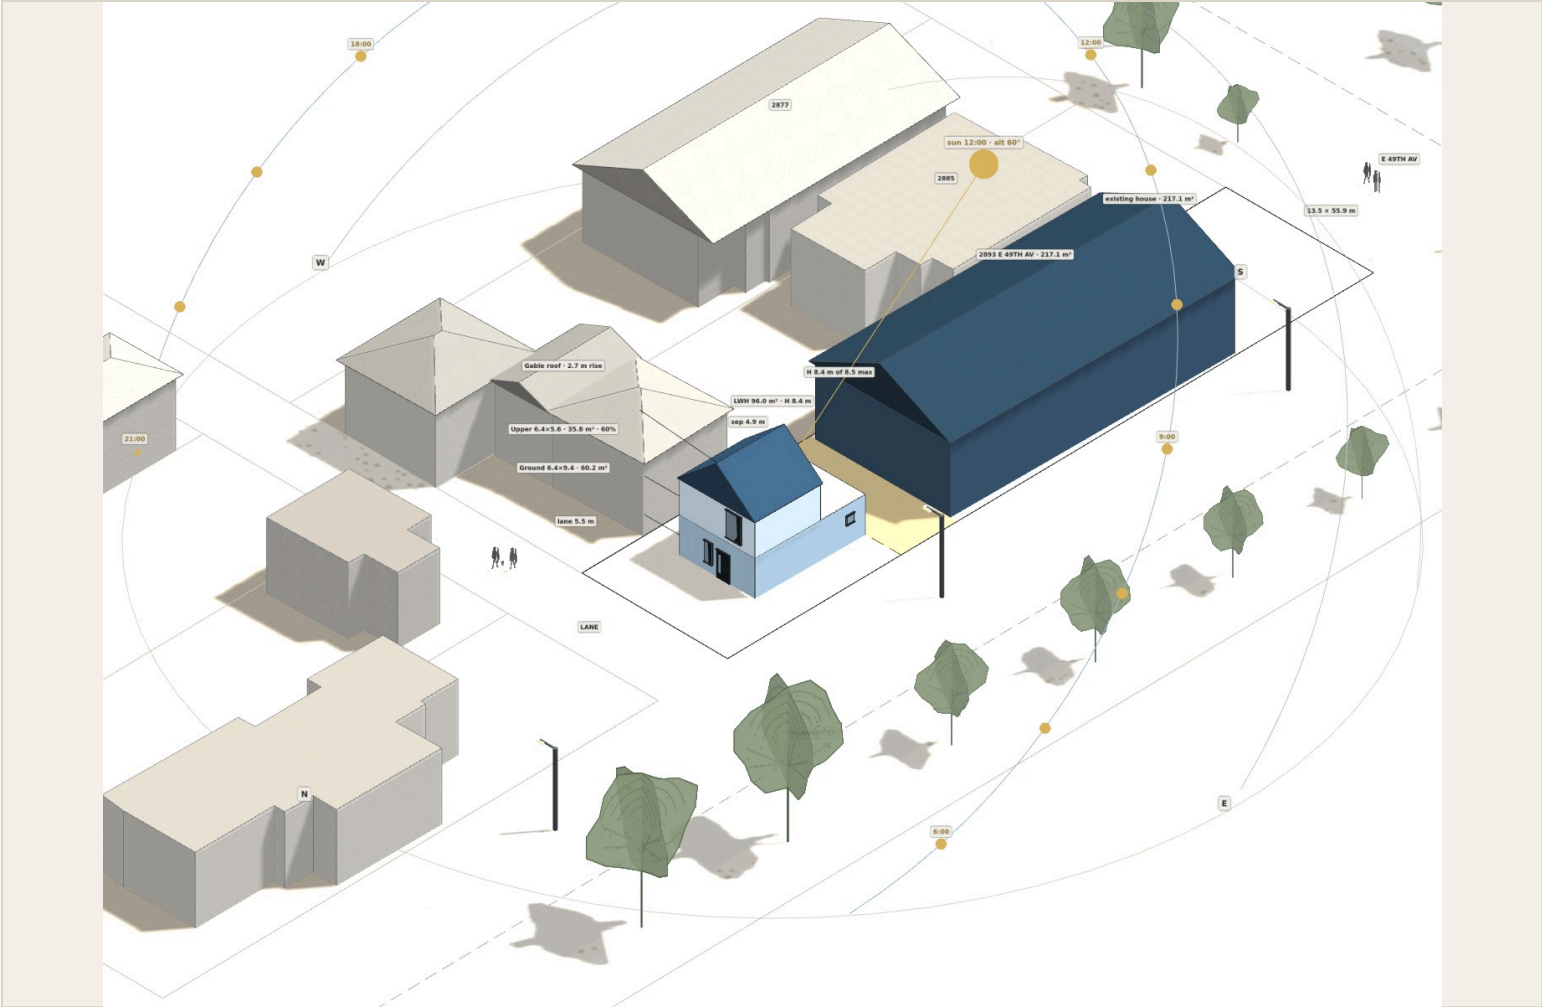

2893 E 49TH AV · 96.0 m² · gable (ridge along depth) roof

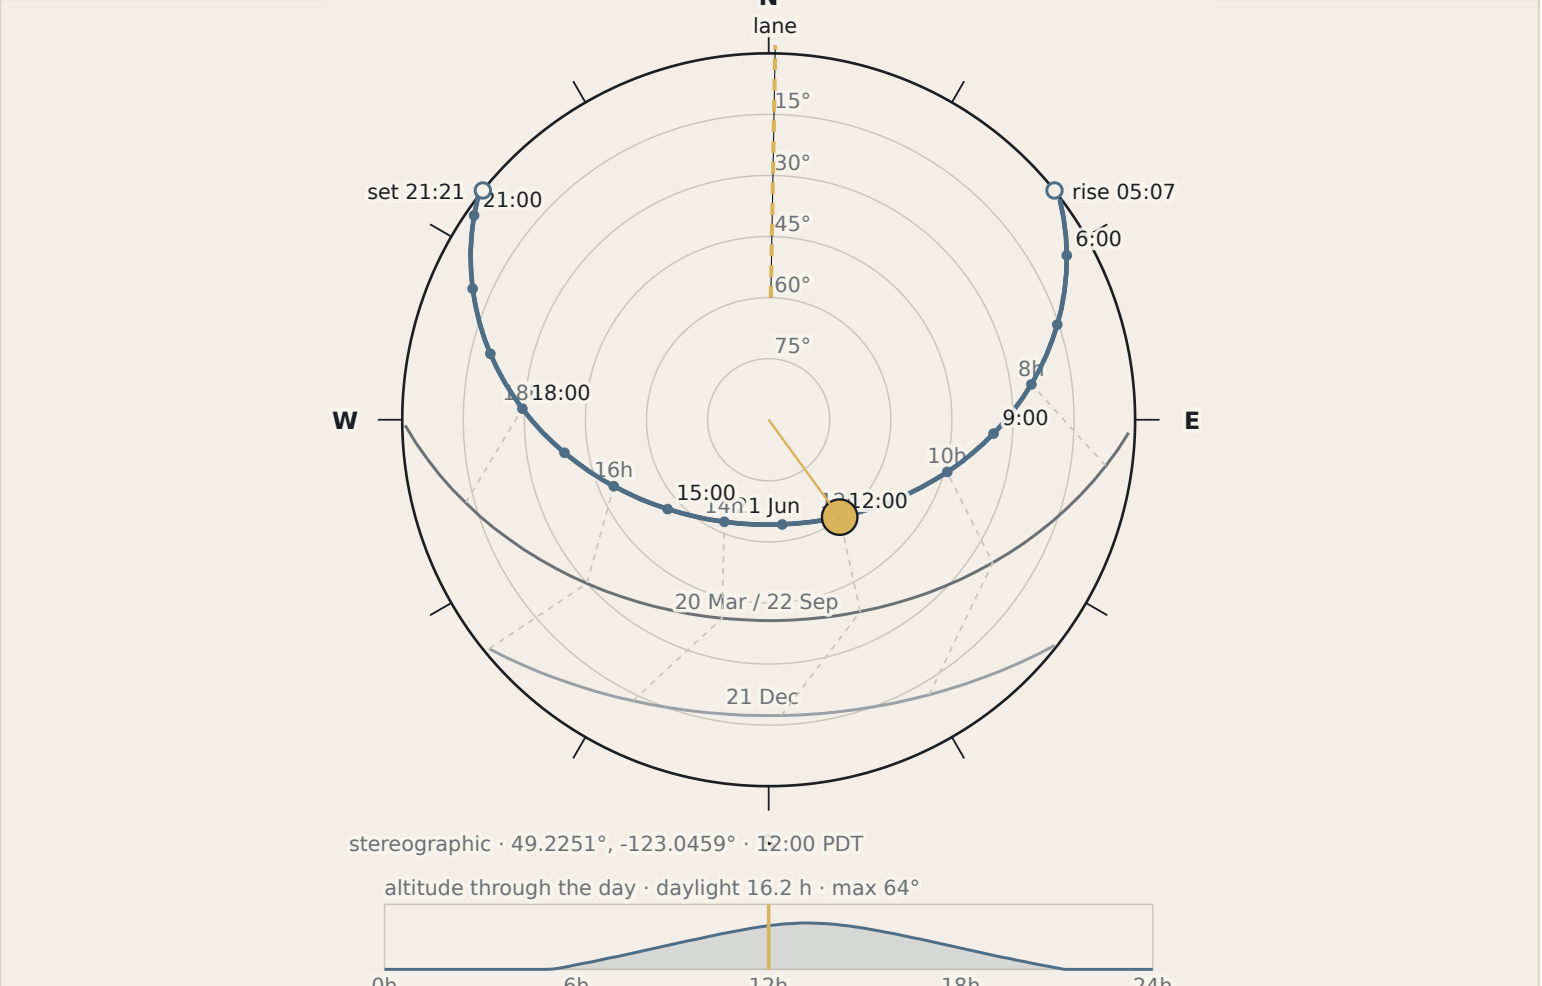

STATUS	REQUIREMENT	MEASURED	CLAUSE	NO.	WALL	TYPE	SIZE	SILL
Meets	Site is viable for a laneway house: R1-1, single detached house, vehicular access from a rear lane, no laneway house already on the site	Viable lot – R1-1, lane at the rear, no structure on record behind the house – Corner lot – a street runs along one side; s.11.3.8.6(c) side setbacks still apply to both side property lines, and the flanking street frontage may carry extra design guidance.	s.11.3.8.1; R1-1 s.2.1	#1	Lane · ground	door	1.0 × 2.1 m	–
				#2	Lane · ground	fixed	0.6 × 1.5 m	0.8 m
				#3	Lane · upper	fixed	1.2 × 2.0 m	0.5 m
				#4	Left · upper	casement	0.9 × 0.9 m	1.1 m
				#5	Left · ground	casement	0.9 × 0.9 m	1.2 m
Meets	Laneway house at least 4.9 m from the single detached house, measured across the site	4.9 m	s.11.3.8.6(a)	#6	Left · upper	casement	0.9 × 0.9 m	1.1 m
				#7	Left · ground	casement	0.9 × 0.9 m	1.2 m
Meets	At least 0.9 m from the ultimate rear (lane) property line	5.5 m	s.11.3.8.6(b)	#8	Left · ground	casement	0.9 × 0.9 m	1.2 m
Meets	At least 1.2 m from each side property line (Director may reduce on sites under 10.1 m wide)	ground L 3.1 / R 2.9 m · upper L 3.1 / R 2.9 m	s.11.3.8.6(c)	#9	Street side · ground	slider	2.4 × 2.1 m	0.1 m
				#10	Street side · upper	casement	1.2 × 1.5 m	0.9 m
Meets	Building height not more than 8.5 m (gable (ridge along depth) roof adds 2.7 m above 5.7 m walls)	8.4 m total	s.11.3.8.4	#11	Right · ground	awning	0.6 × 0.6 m	1.6 m
Meets	Floor area not more than the lesser of 0.25 × site area (175.3 m²) and 186 m² – 0.25 × site governs here	96.0 m² · FSR 0.14	s.11.3.8.2					
Meets	Site coverage with a laneway house not more than 50% of site area (house footprint + laneway ground floor)	39.5%	s.11.3.8.5; R1-1 s.3.2.2.7					
Meets	Minimum site width 9.8 m (Director may reduce for sites at least 7.3 m wide)	13.5 m	s.11.3.8.3					
Meets	Upper floor not more than 60% of ground floor (36.1 m²)	35.8 m² = 60% of ground	Brief rule					
Meets	All laneway volumes within the property lines of the surveyed parcel	within lot	geometry					
Note	Floor-to-floor over 3.7 m adds the floor area below the excess height to the laneway floor area	3.0 / 2.7 m	s.11.3.8.8(c)					
Note	Two storeys need workable storey heights; roof form determines wall height under the 8.5 m cap	3.0 / 2.7 m	Design note					
Note	Laneway house permit requires 1 tree retained or planted in the front yard (site under 15.1 m wide)	0 public tree(s) at the frontage	R1-1 s.2.2.1; s.2.2.2					
Note	Laneway house permitted only with a single detached house on a site with vehicular access from the rear; conditional approval use	existing footprint used · rear: LANE	s.11.3.8.1; R1-1 s.2.1					
Note	Laneway floor area is excluded from the main house FSR; laneway house is regulated by Section 11, not R1-1 sections 3–4	96.0 m² excluded	R1-1 s.4.1.2(a); s.2.2.4					
Note	No decks or roof decks above the uppermost level of a laneway house	roof only	s.11.3.8.10					